


KANGWA E. MUKUKA - 12A/R
MPELEMBE SEC SCHOOL
EXAM NO.: 1750270053
CENTRE NO.: 5027

VINTAGE LED LIGHT-UP SIGN

(ELECTRONIC WOODEN SIGN)


WORKING DRAWING
DWG NO.05 - BLUEPRINT OF ARTEFACT
THUR 23RD SEPT, 2020
PAGE NO. 34

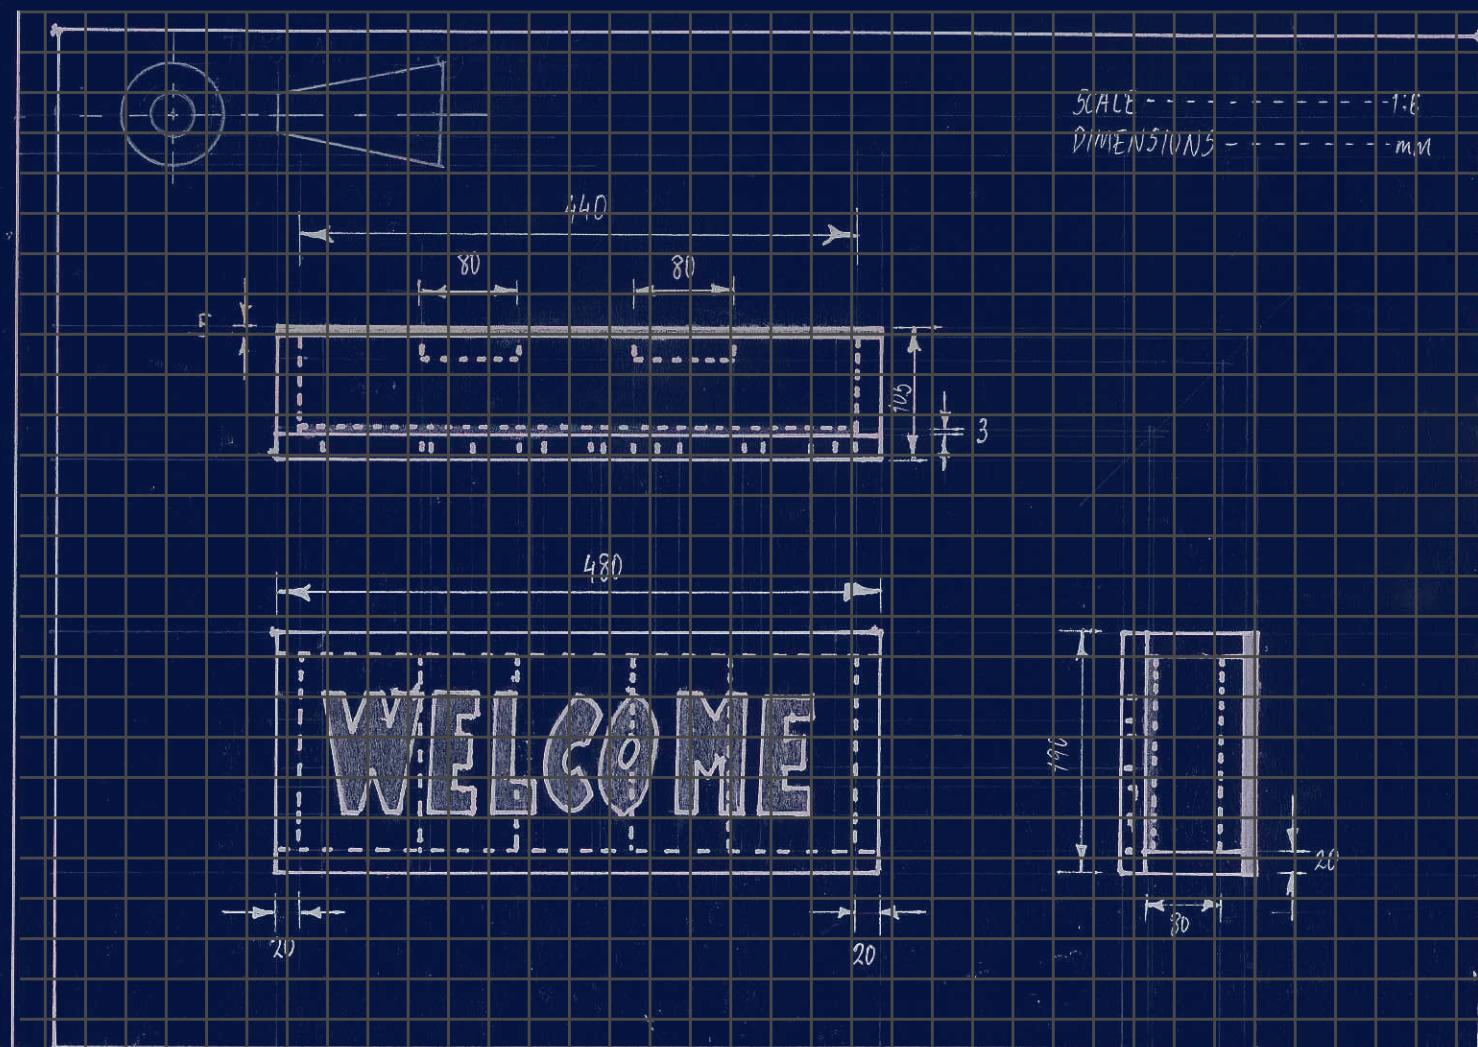

SCALE 1:8
DIMENSIONS mm

Total Surface Area
Volume

$3.732 \times 10^5 \text{ mm}^2$ or 3.732 cm^2
 $5.28 \times 10^9 \text{ mm}^3$ or 5.280 cm^3

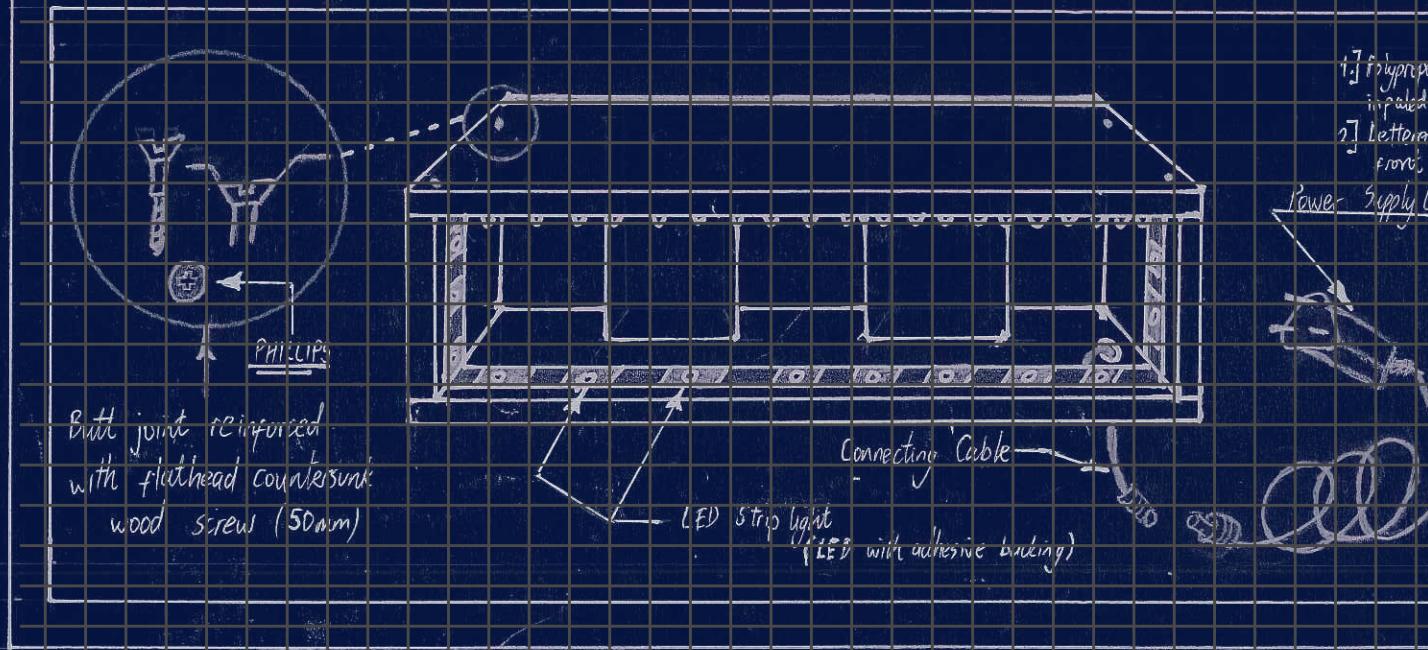

- 1] Polypropylene screen put before impaled pinewood.
- 2] Lettered pinewood fixed to front elevation (F)

